


ESTE PLANO ES DE PROPIEDAD DE MINERA LOS PELAMBRES.  
SU REPRODUCCION ESTA PROHIBIDA, EXCEPTO  
EXPRESA AUTORIZACION POR PARTE DE LA EMPRESA.

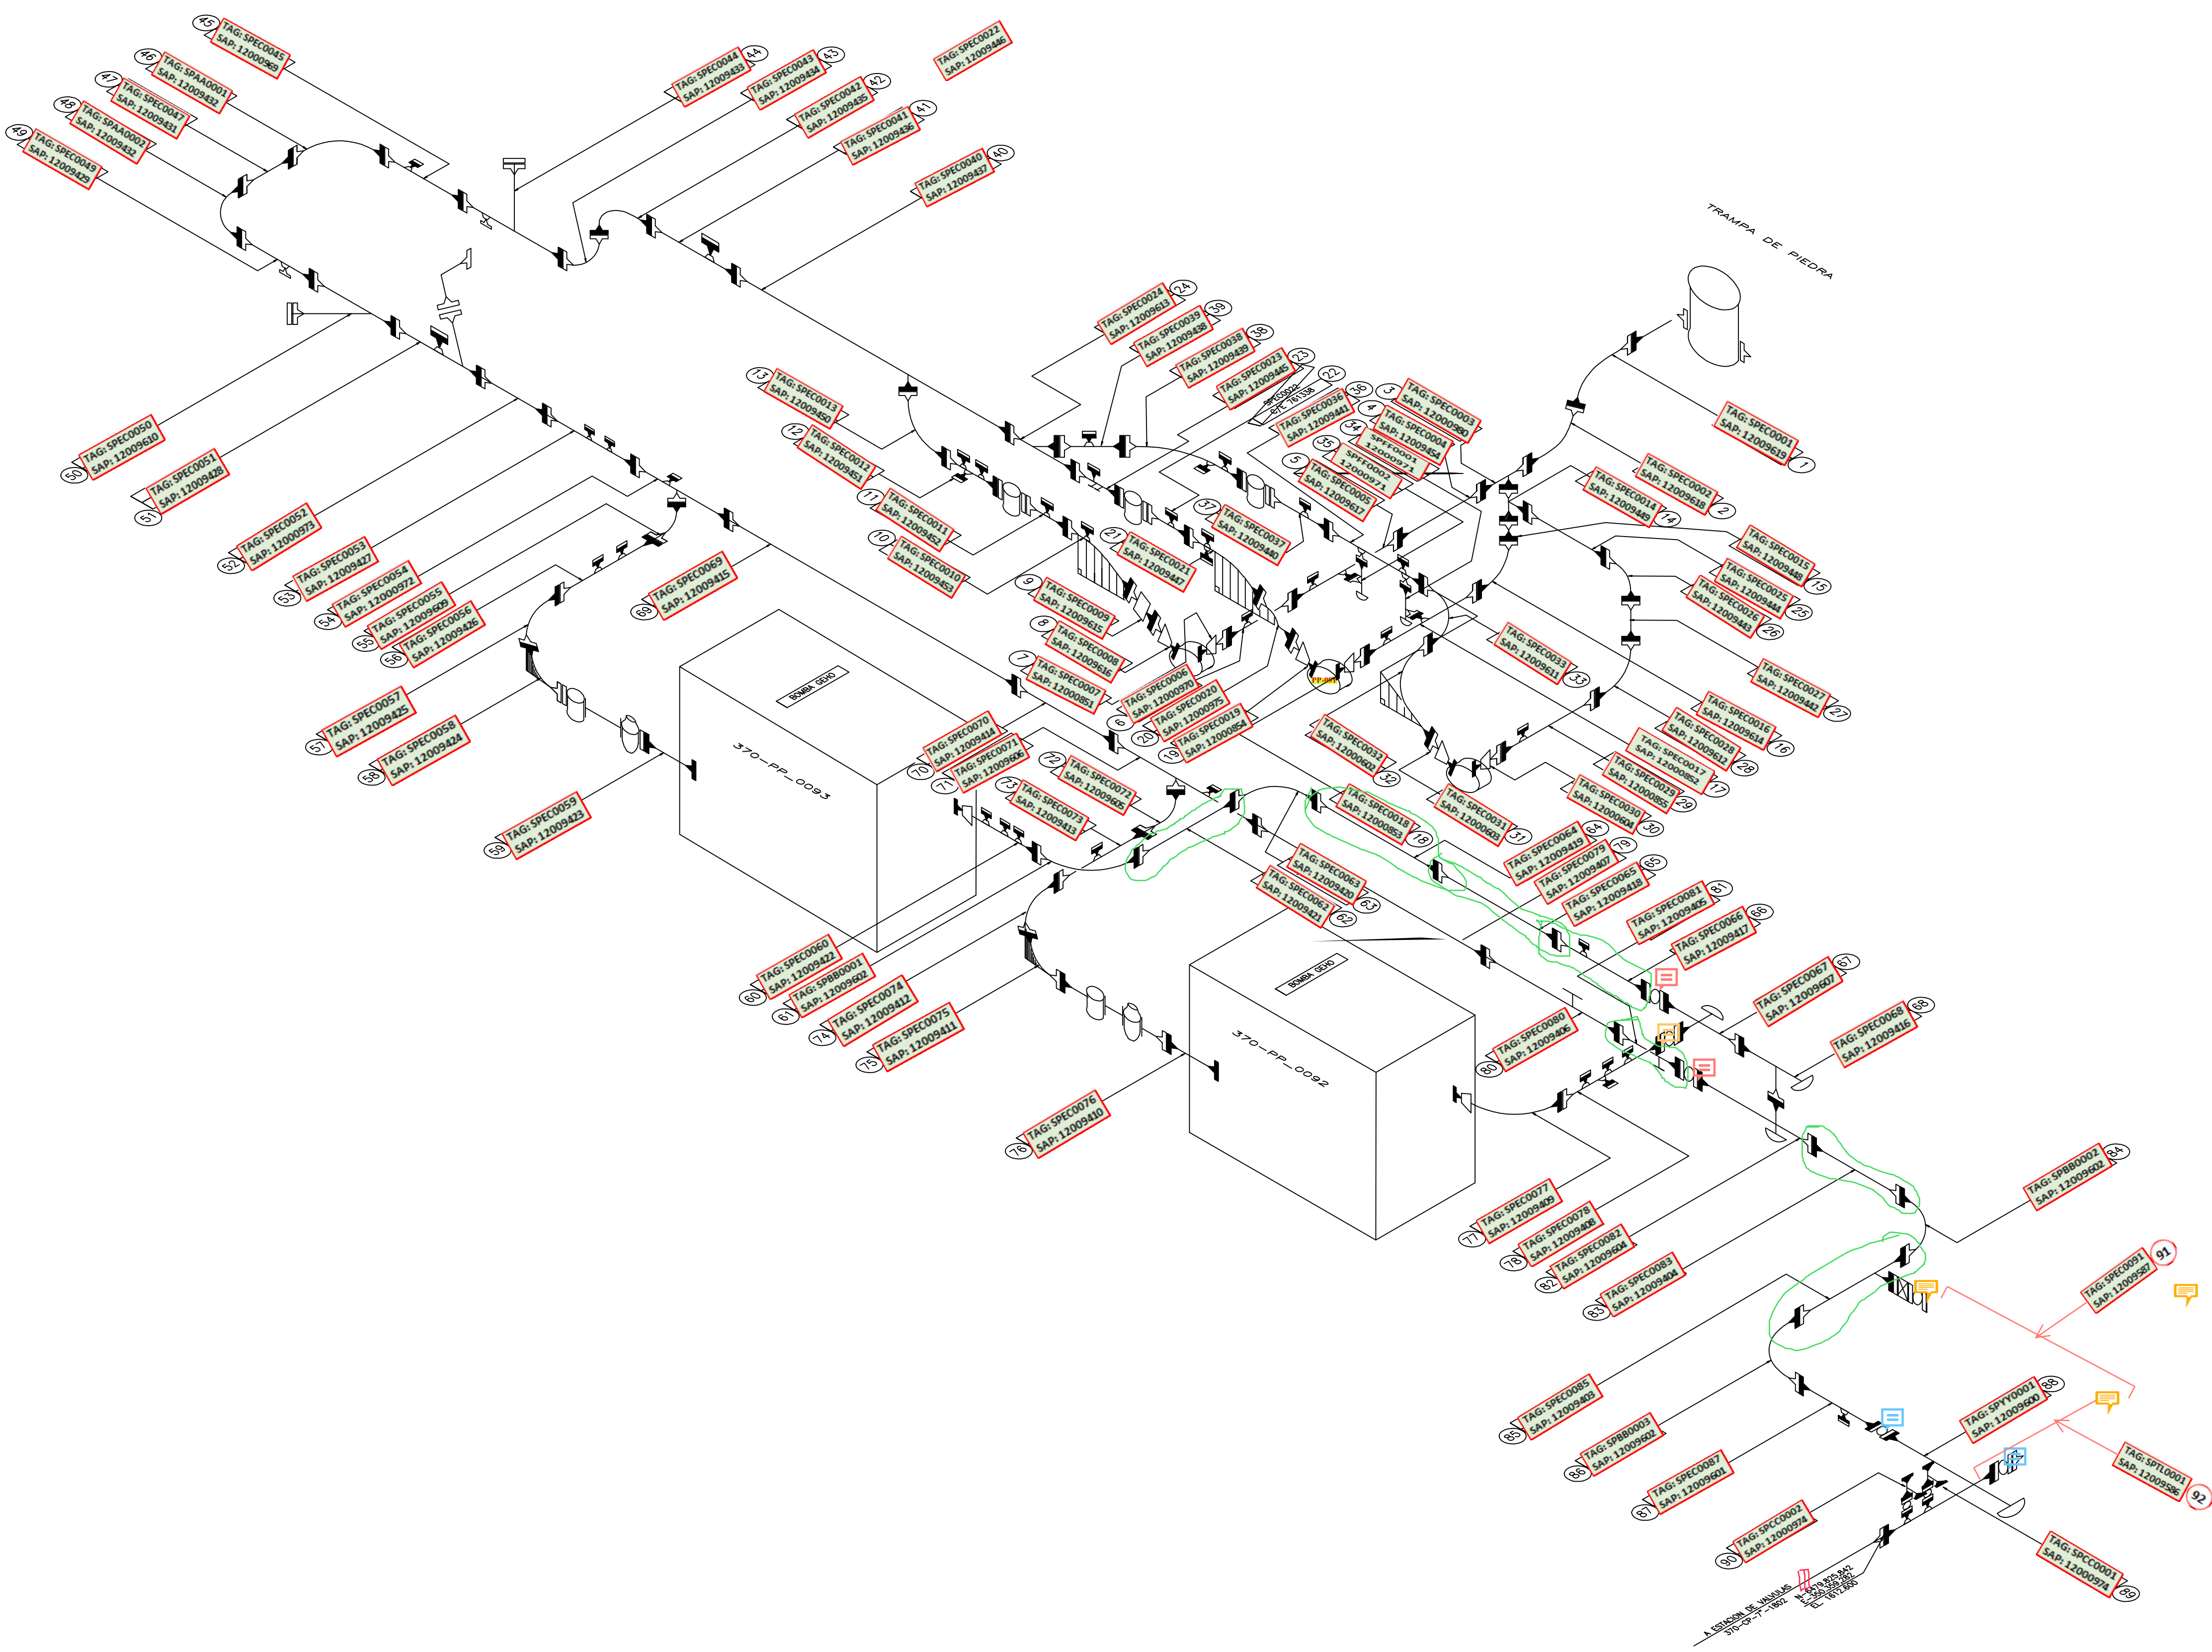

# ESTACION DE BOMBAS



MINERA  
LOS PELAMBRES

|        | NOMBRE | FECHA    |
|--------|--------|----------|
| DISEÑO | G.O.P. | 04-04-13 |
| REVISO | M.A.O. | 04-04-13 |
| APROBO | C.N.B  | 04-04-13 |

MINERA LOS PELAMBRES  
ESTACION DE BOMBAS  
CONCENTRADUCTO

LAYOUT ISOMETRICO  
KM 0

MATERIAL  
INDICADOS

N° PLANO  
370-ISO-01

LAMINA 1 DE 1  
CODIGO PRODUCTO

ESCALA  
S/E  
REV.  
0