


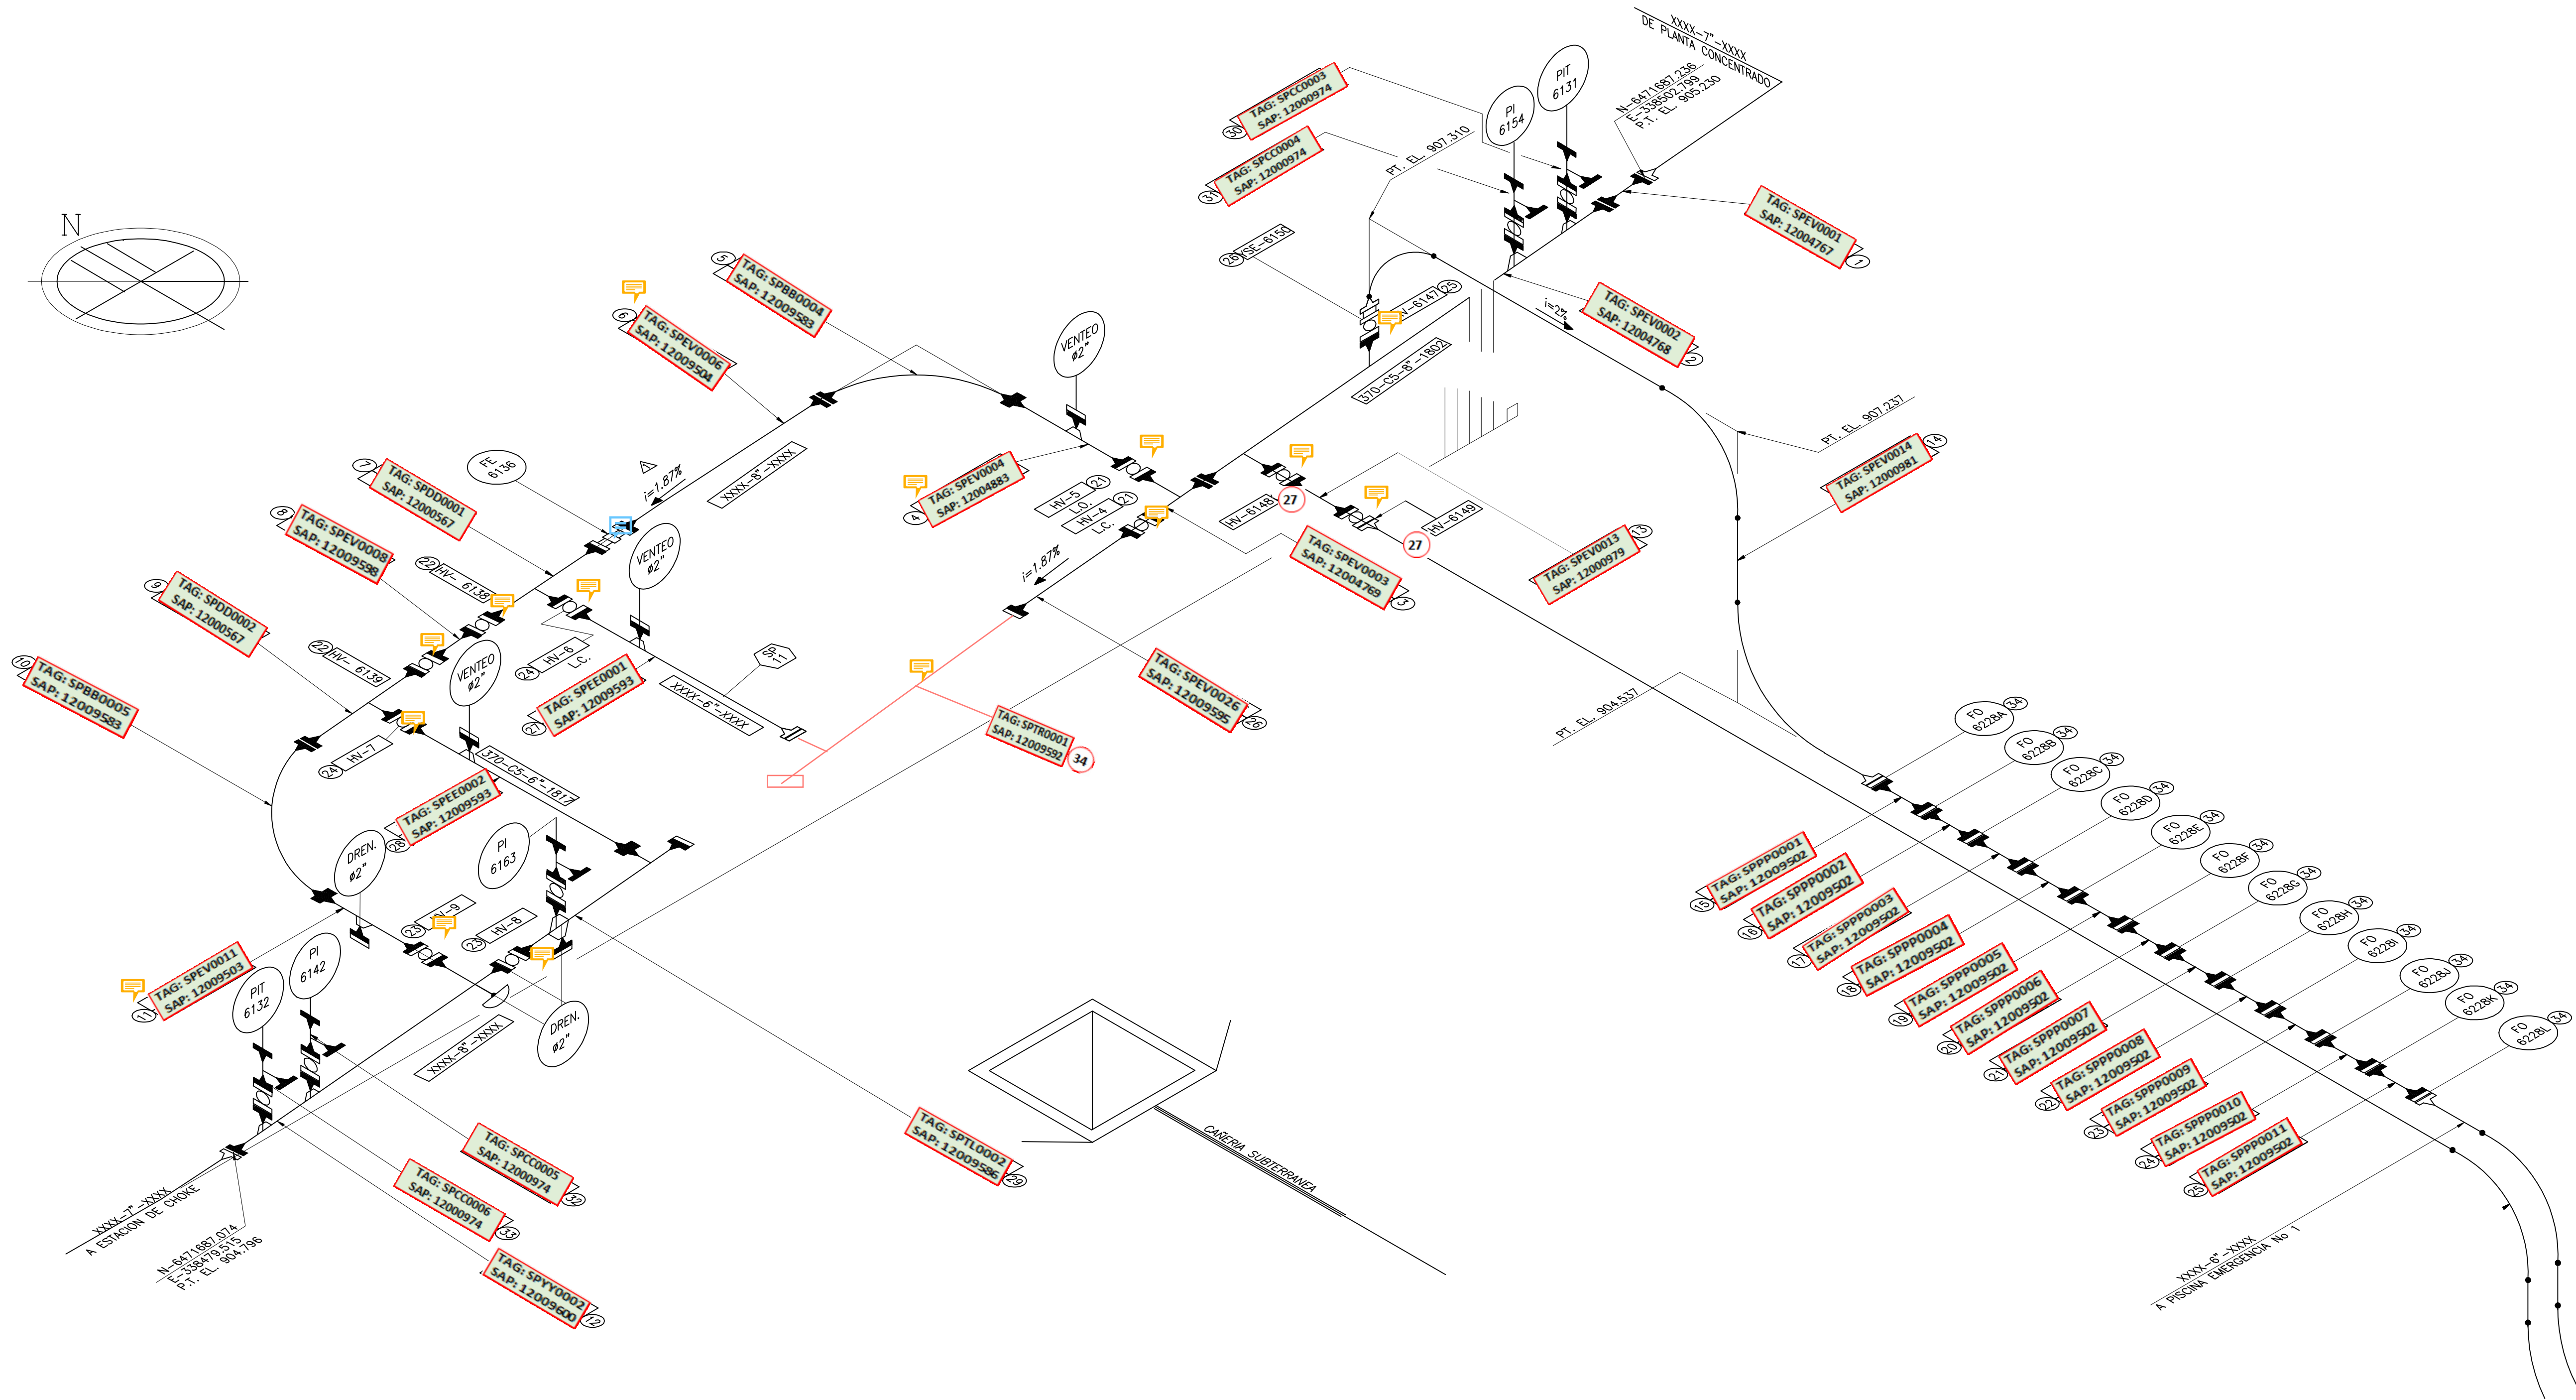

ESTACION DE VALVULAS

			MINERA LOS PELAMBRES ESTACION DE VALVULAS CONCENTRADUCTO		MATERIAL INDICADOS	
					N° PLANO 370-ISO-02	
			LAYOUT ISOMETRICO KM 22		LAMINA 1 DE 1	ESCALA S/E
					CODIGO PRODUCTO	REV. 0
	DISEÑO	G.O.P.	04-04-13			
	REVISO	M.A.O.	04-04-13			
	APROBO	C.N.B.	04-04-13			