


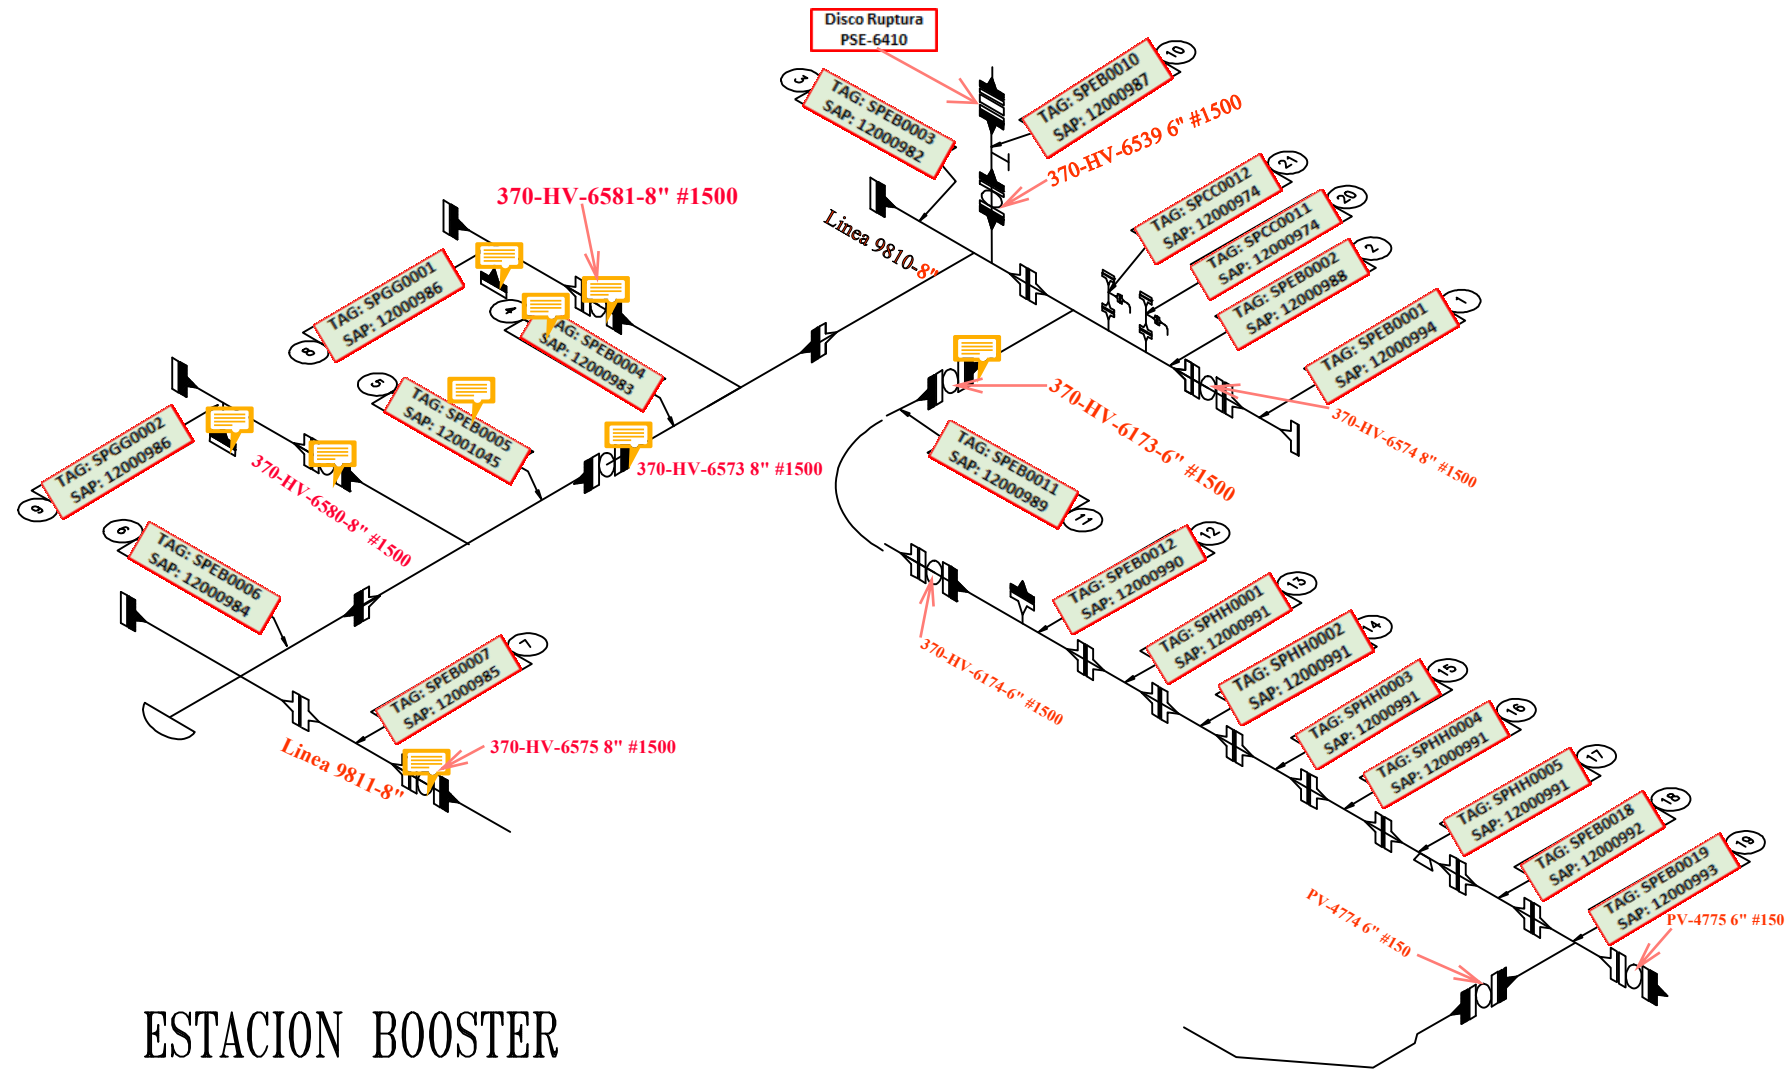

ESTACION BOOSTER
km 80



	NOMBRE	FECHA
DISENO	G.O.P.	04-04-14
REVISO	M.A.O.	04-04-14
APROBO	C.N.B.	04-04-14

MINERA LOS PELAMBRES
ESTACION BOOSTER
CONCENTRADUCTO

LAYOUT ISOMETRICO
KM 80

INDICADOS	
N° PLANO	0370-ISO-04
LAMINA 1 DE 1	ESCALA S/E
CODIGO PRODUCTO	REV. 0